
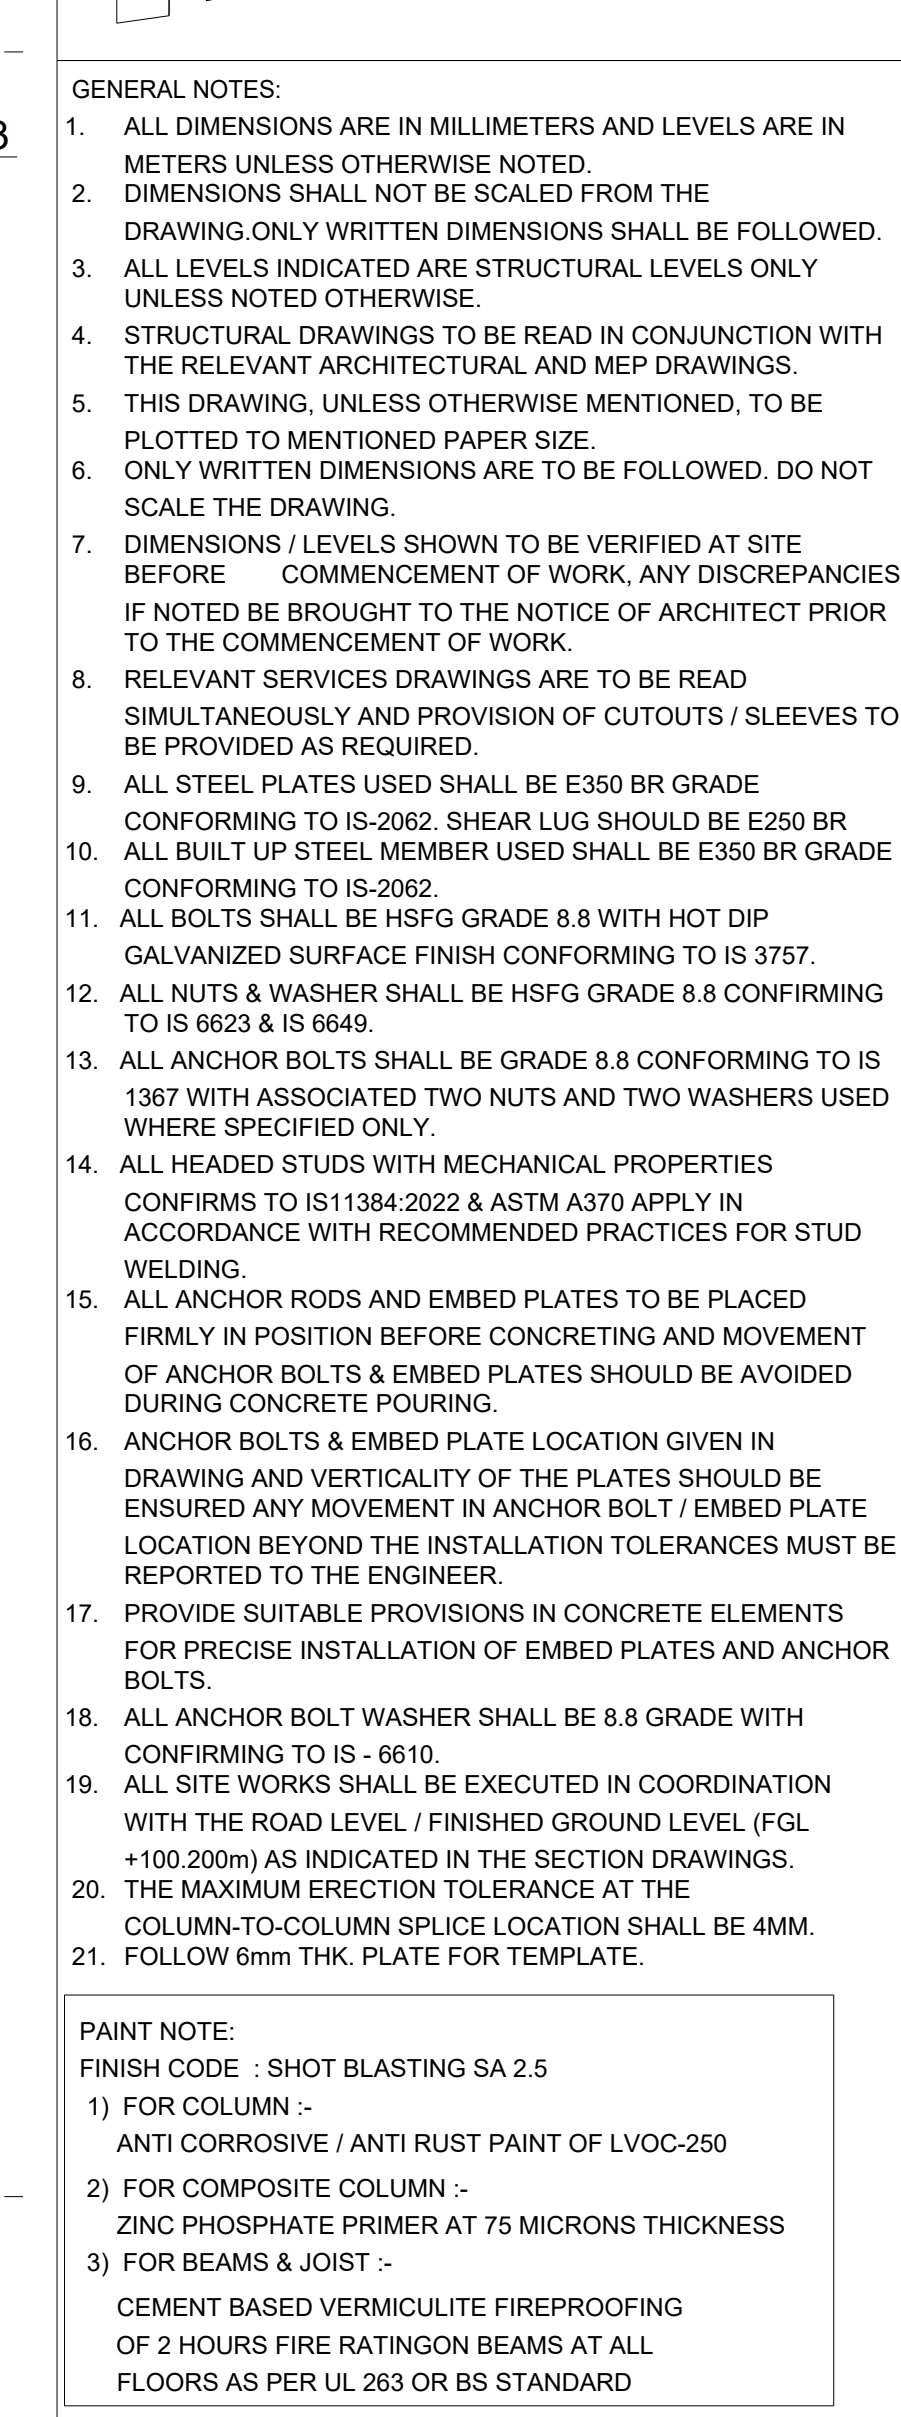
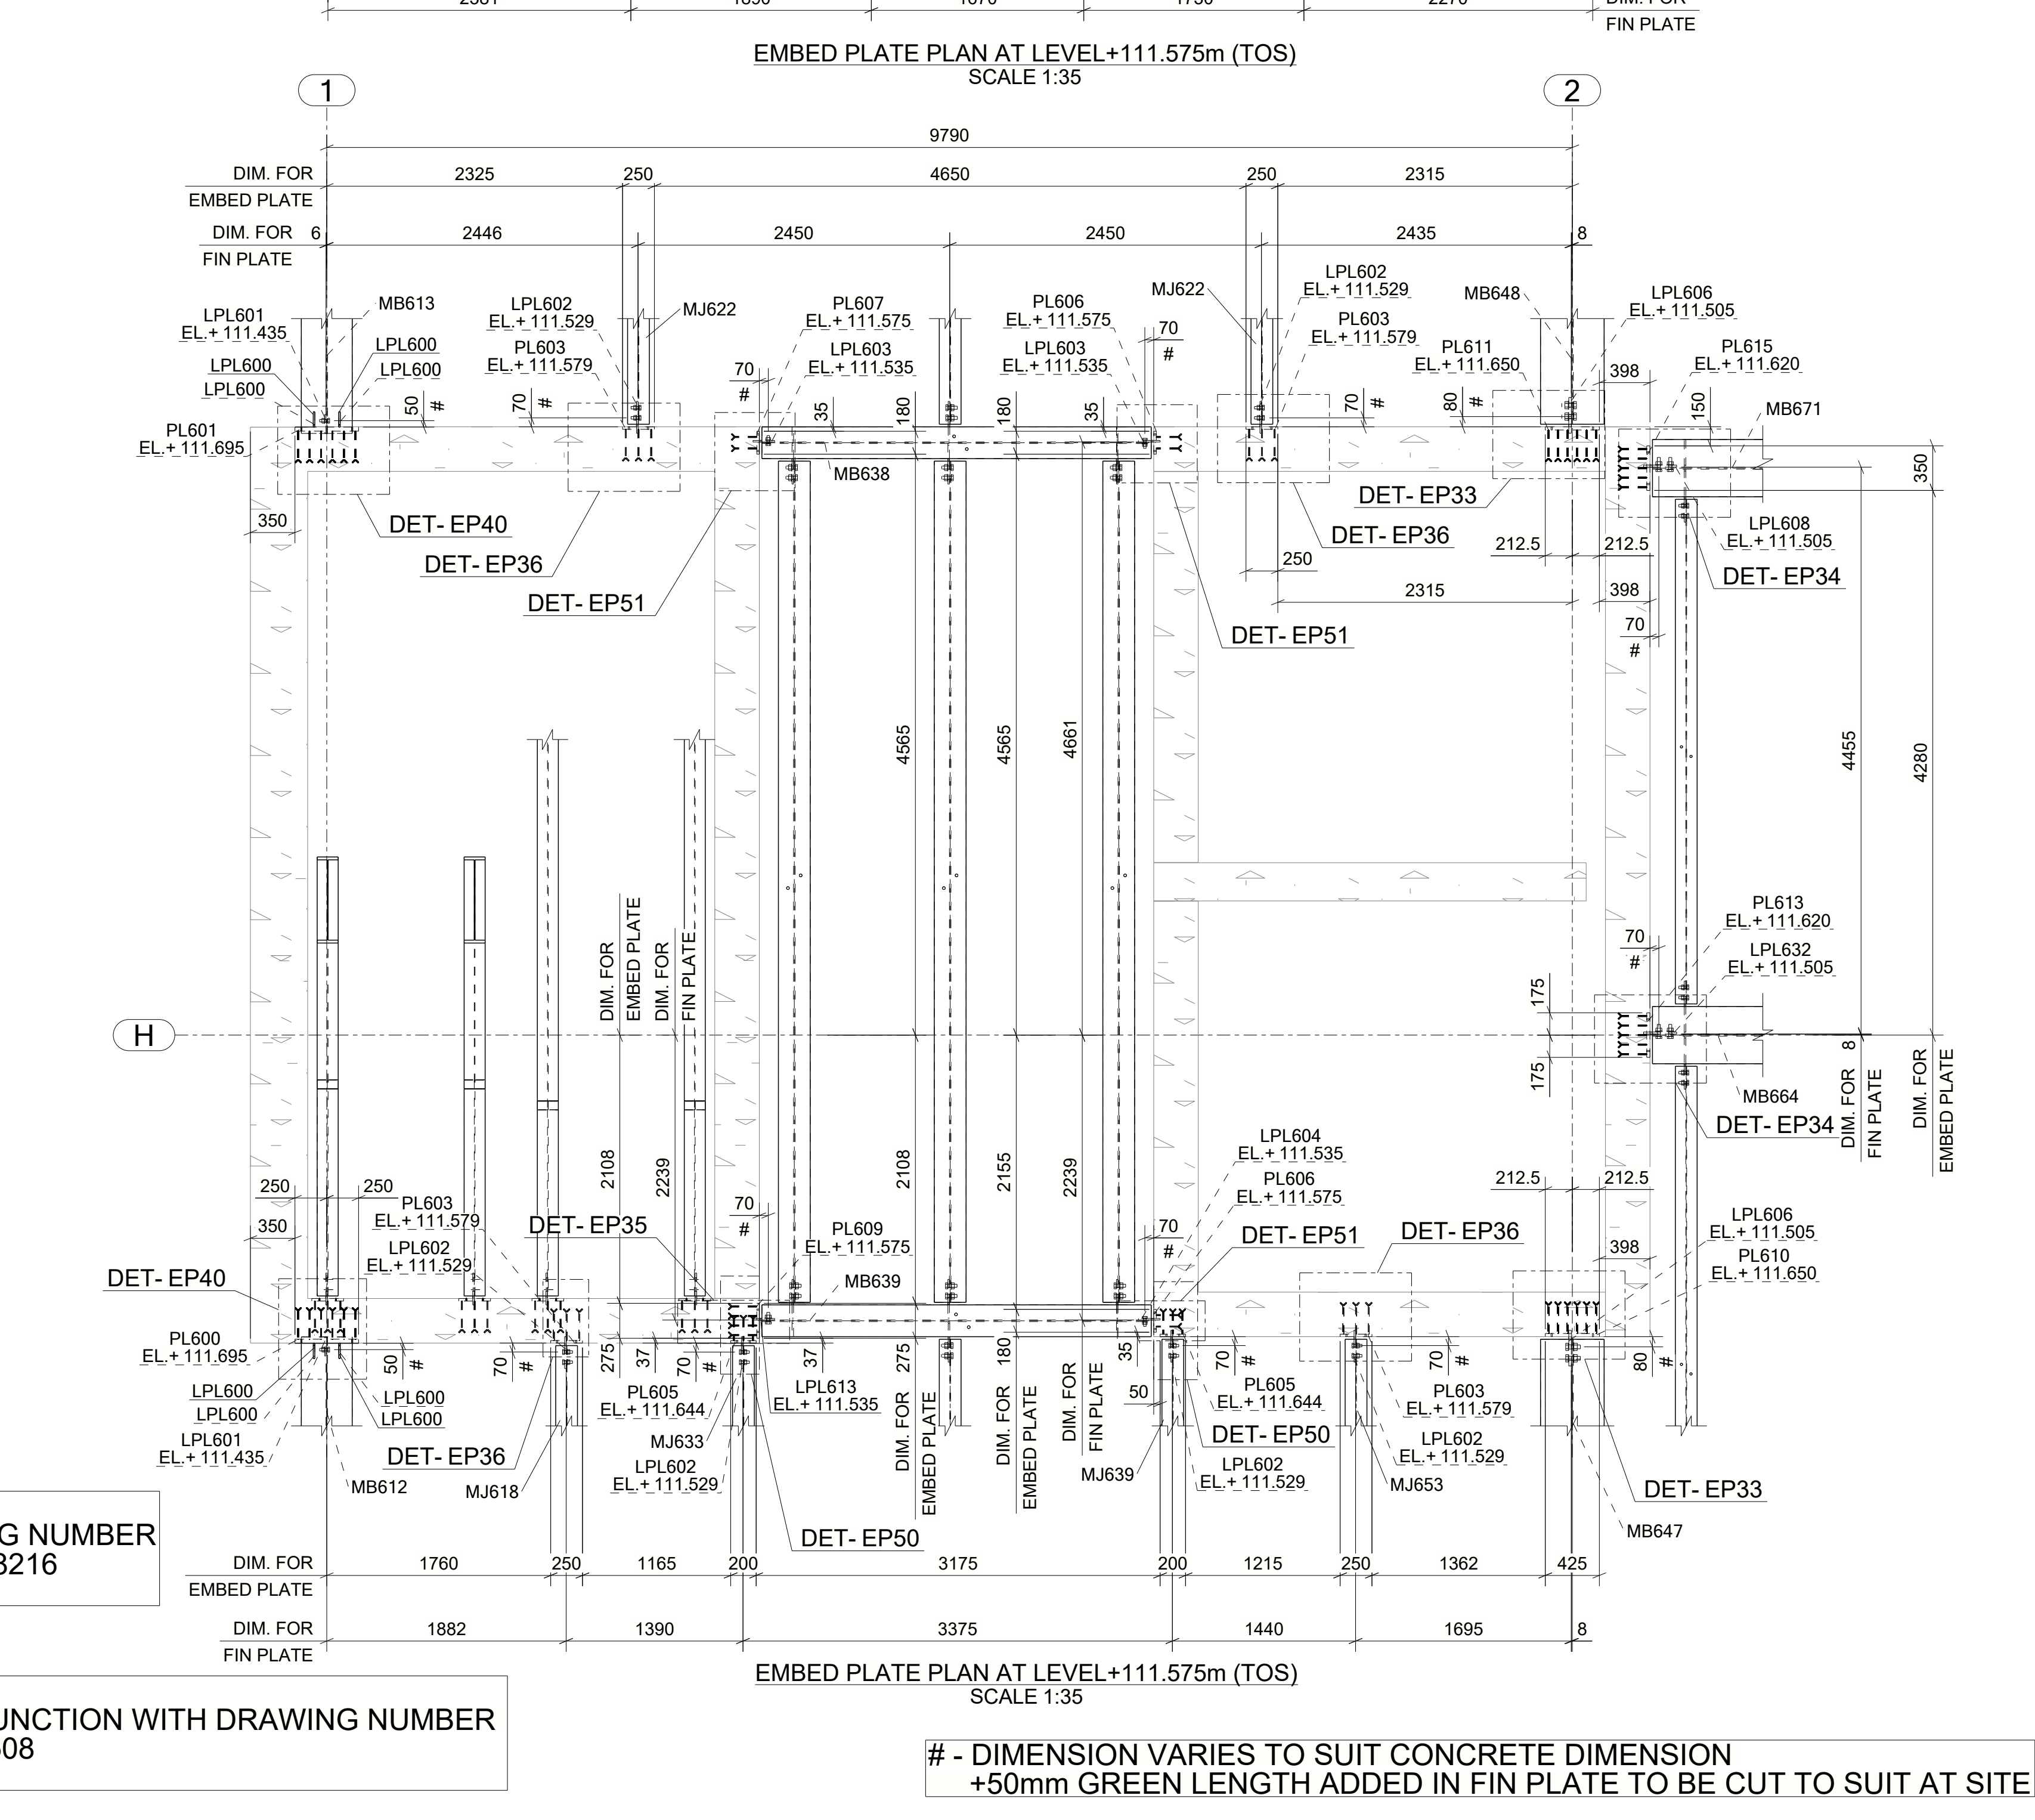


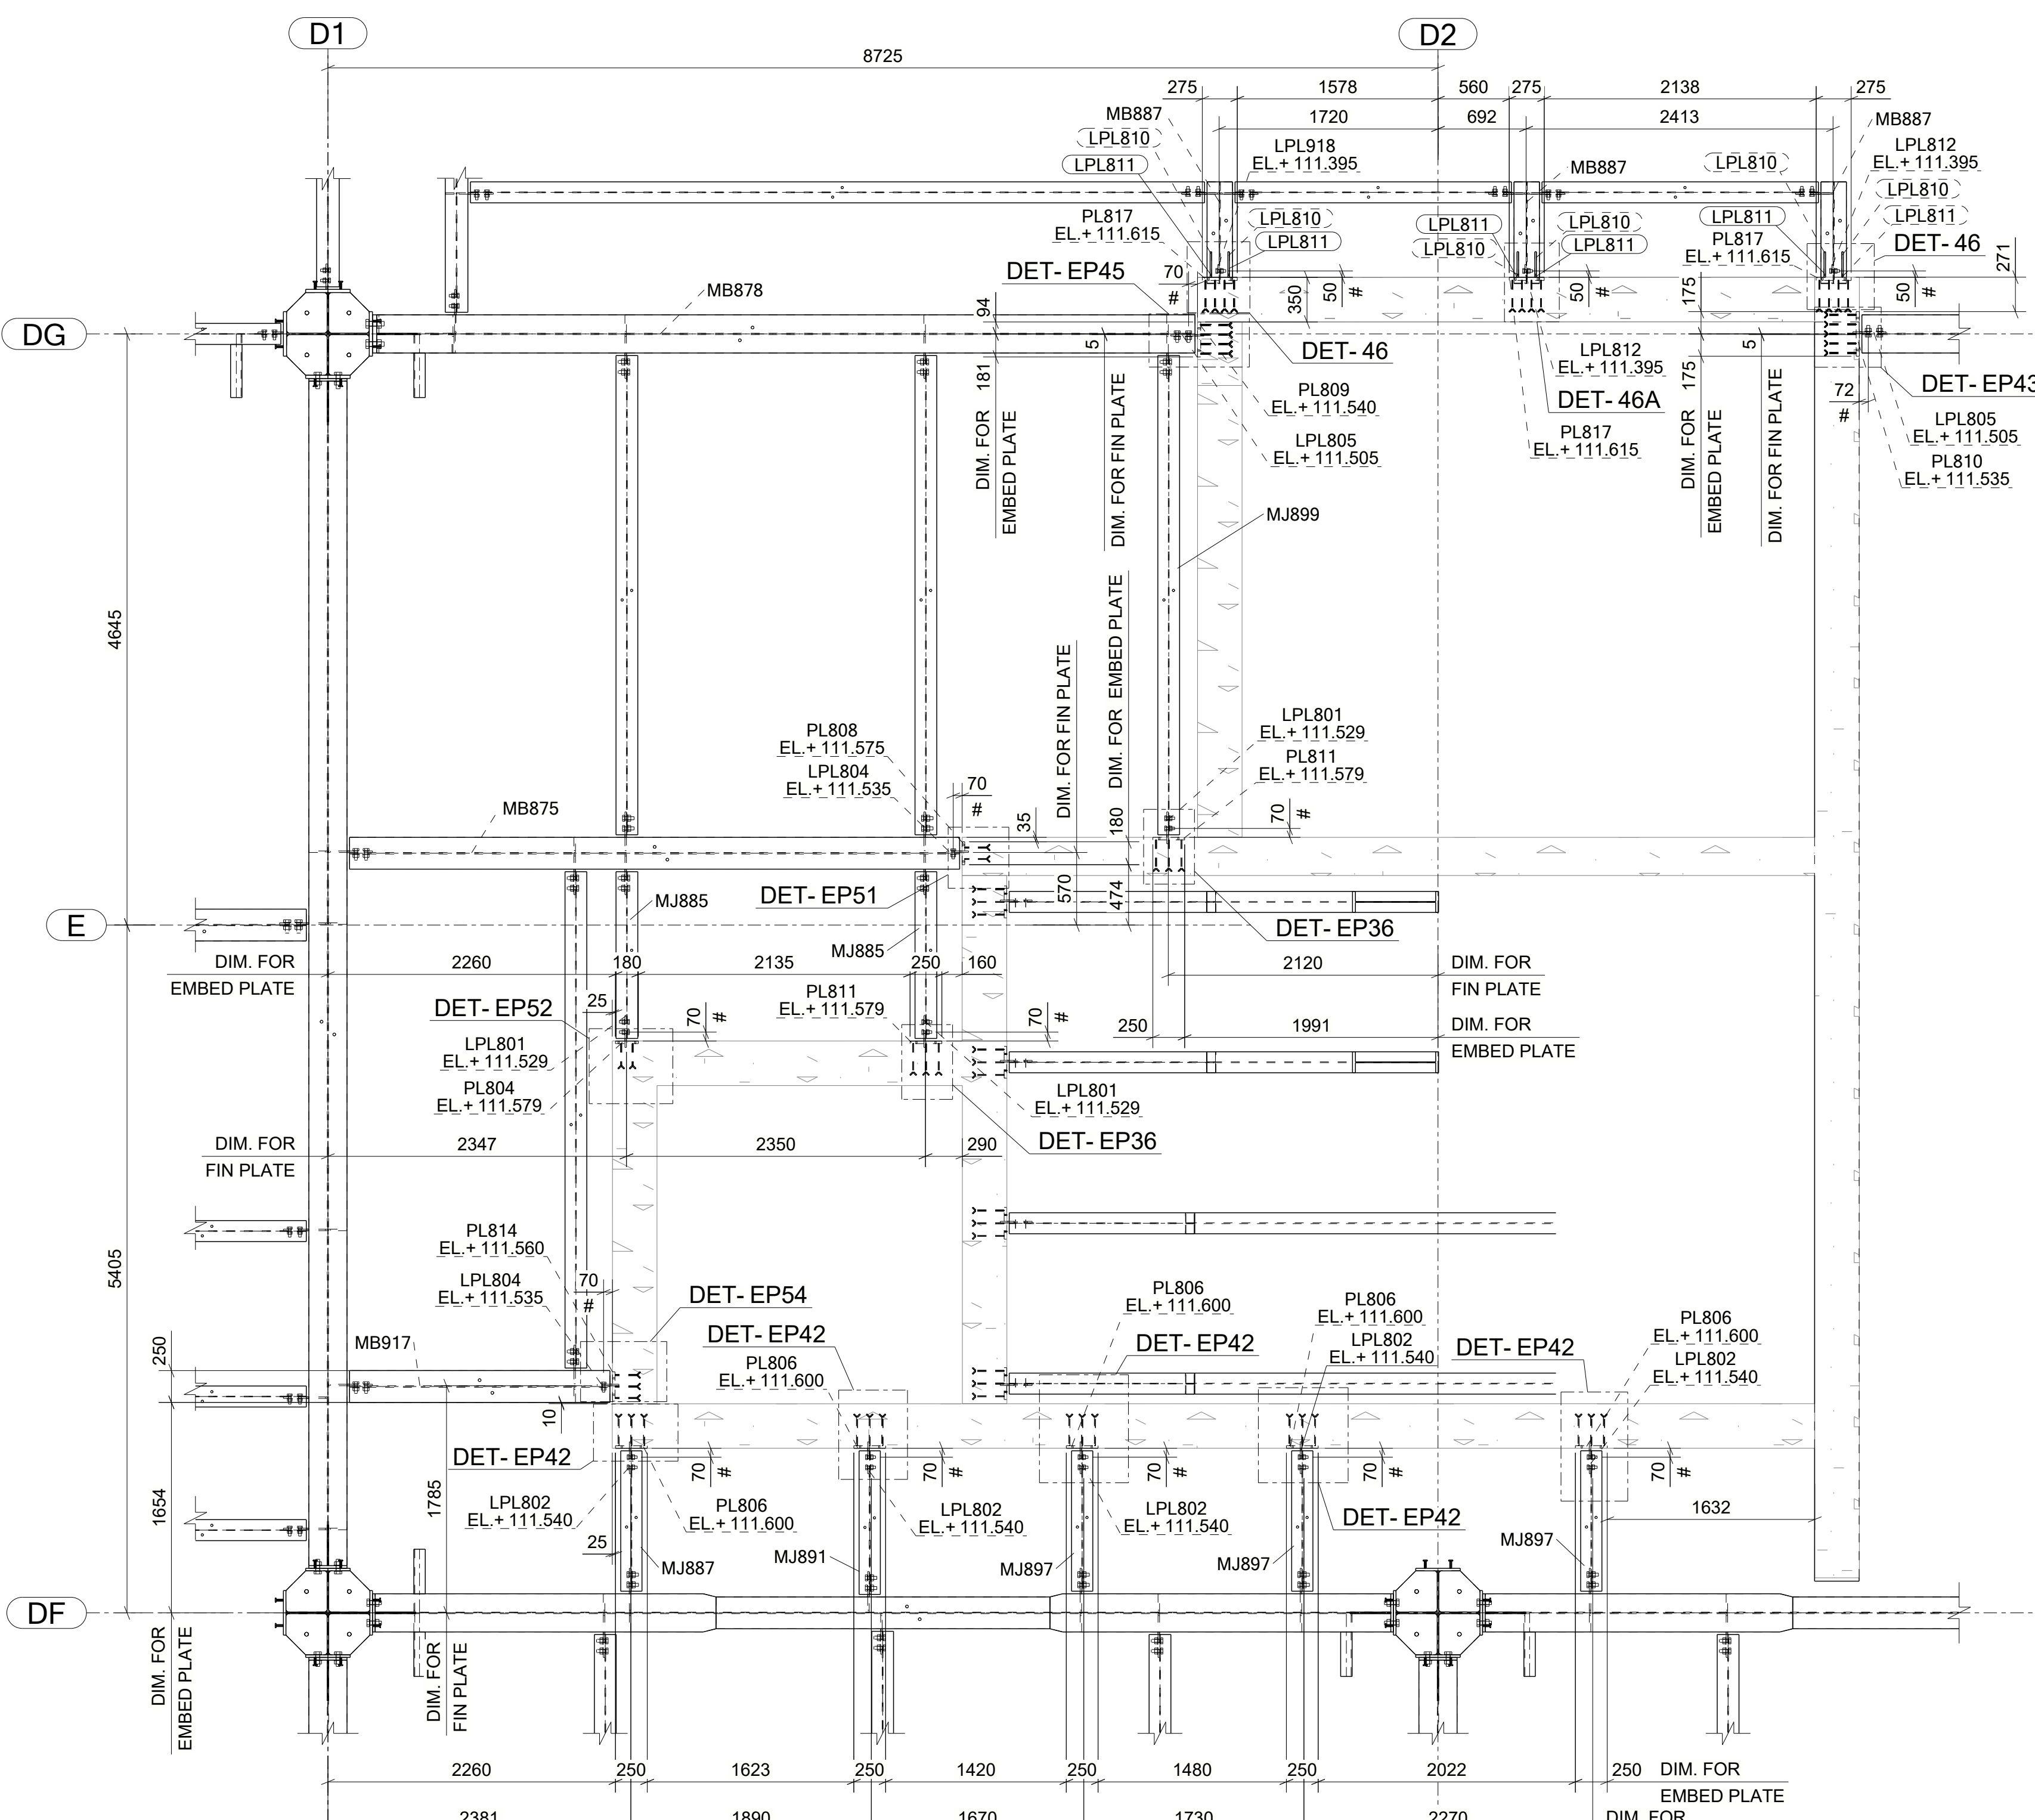

BREVIFICATIONS:			
U N O	- UNLESS NOTED OTHERWISE		
T & B	- TOP & BOTTOM		
T.O.S	- TOP OF STEEL		
B.O.S	- BOTTOM OF STEEL		
T.O.E.P	- TOP OF EMBED PLATE		
B.O.B.P	- BOTTOM OF BASE PLATE		
T.C.P	- TOP OF CONCRETE		
B.C.P	- BOTTOM OF CONCRETE		
PJP	- PARTIAL JOINT PENETRATION GROOVE WELD		
C.J.P	- COMPLETE JOINT PENETRATION GROOVE		
WELD	- HIGH STRENGTH FRICTION GRIP BOLT		
HSFG	- TYPICAL		
E.L	- ELEVATION LEVEL		
- ORIENTATION MARK = EFFECTIVE THROAT OF PJP = LEG SIZE OF FILLET WELD			
R1	30.09.2026	FULLY REVISED	URCTS
R0	26.05.2026	ISSUED FOR CONSTRUCTION	URCTS
REV.	DATE	DESCRIPTION	ISSUED BY
PEER REVIEWER			
 kent cent Kent Data Centres, 8th Floor, R City Offices, Gate No. 3, LBS Marg Chhatrapati Shivaji, Mumbai-400006, Maharashtra, India			
PEER REVIEWER CONTOURS CONSULTING ENGINEERS			
PEER REVIEWER Indian Institute Of Technology Madras IT P.O., Chennai 600 036 INDIA			
DESIGNER CONSULTANT URCTS URCT TECHNOLOGY SERVICES Pvt. Ltd. SHREE ANJANULY CHETTY BUILDING, 3rd THIRD FLOOR, OLD HAJI NEW #58 THIRUMALA PELLAI ROAD-T.NAGAR,CHENNAI-600 017 (INDIA)			
CLIENT: colt Data Centre Services DCHI -Cost Data Centre Services Plot No. 5 & 6A, Kalasa Industrial Area, MIDC, Thane District, Near Airoli, Near Mumbai, Maharashtra, INDIA www.coltdatacentres.net			
PROJECT NAME: COLT DATA CENTRE, MUMBAI MUMD-DC3			
DRAWING TITLE: STRUCTURE - DC3 & DG3 LEVEL 02-STRUCTURAL EMBED PLATE PLAN			
STATUS:			
DESIGNED:	DRAWN:	CHECKED:	SCALE:
MK	NMN	MSS	1:10 1:35
DRAWING NUMBER:			SIZE:
MUMTH-URCT-ZZ-02-DR-S-38207			1189x841
			REVISION R